


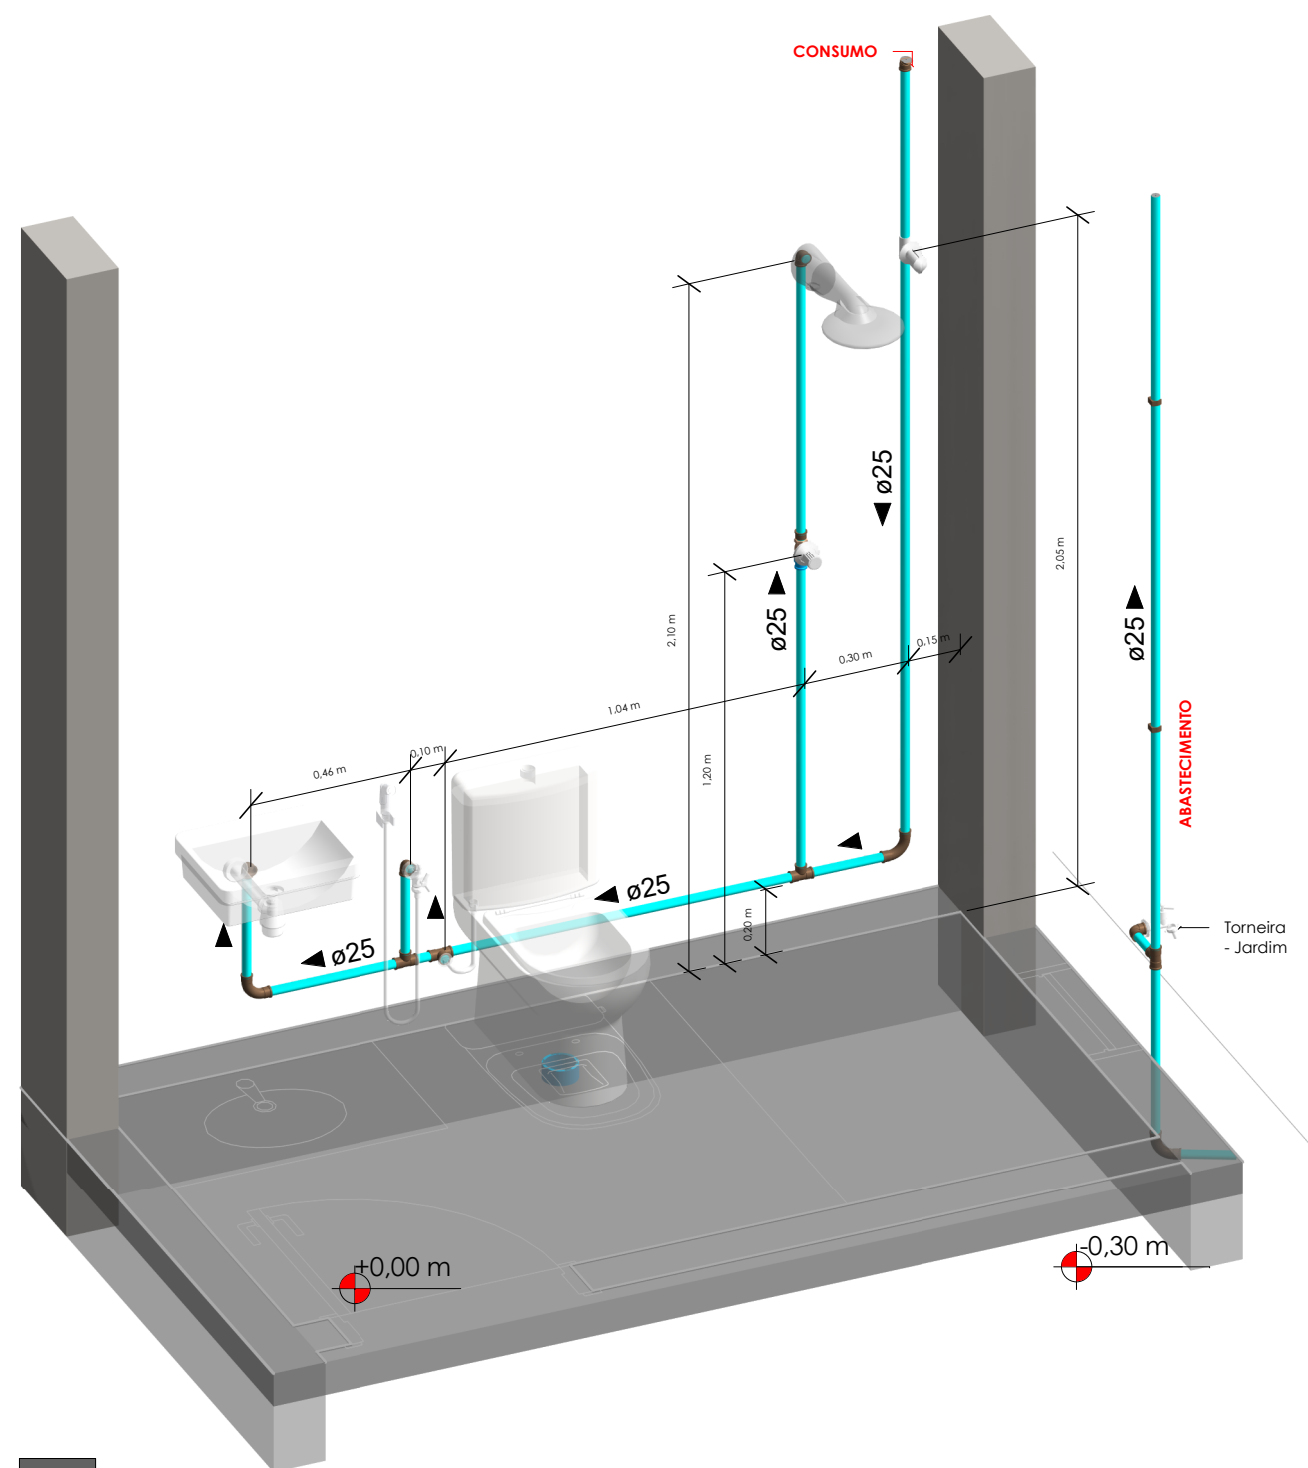


ISOMÉTRICA 01 - BWC GUARITA - ESC

1/20

LEGENDA:

- TUBULAÇÃO PVC BRANCO - ESGOTO
- TUBULAÇÃO PVC BRANCO SN - VENTILAÇÃO ESGOTO
- TUBULAÇÃO PVC MARROM - ÁGUA FRIA
- AL- $\frac{nn}{\varnothing xx}$ -ALIMENTAÇÃO DO RESERV. SUPERIOR
nn: número da coluna
xx: diâmetro nominal da coluna
- CV- $\frac{nn}{\varnothing xx}$ -COLUNA DE VENTILAÇÃO
nn: número da coluna
xx: diâmetro nominal da coluna
- AF- $\frac{nn}{\varnothing xx}$ -COLUNA DE ÁGUA FRIA (BARRILETE)
nn: número da coluna
xx: diâmetro nominal da coluna

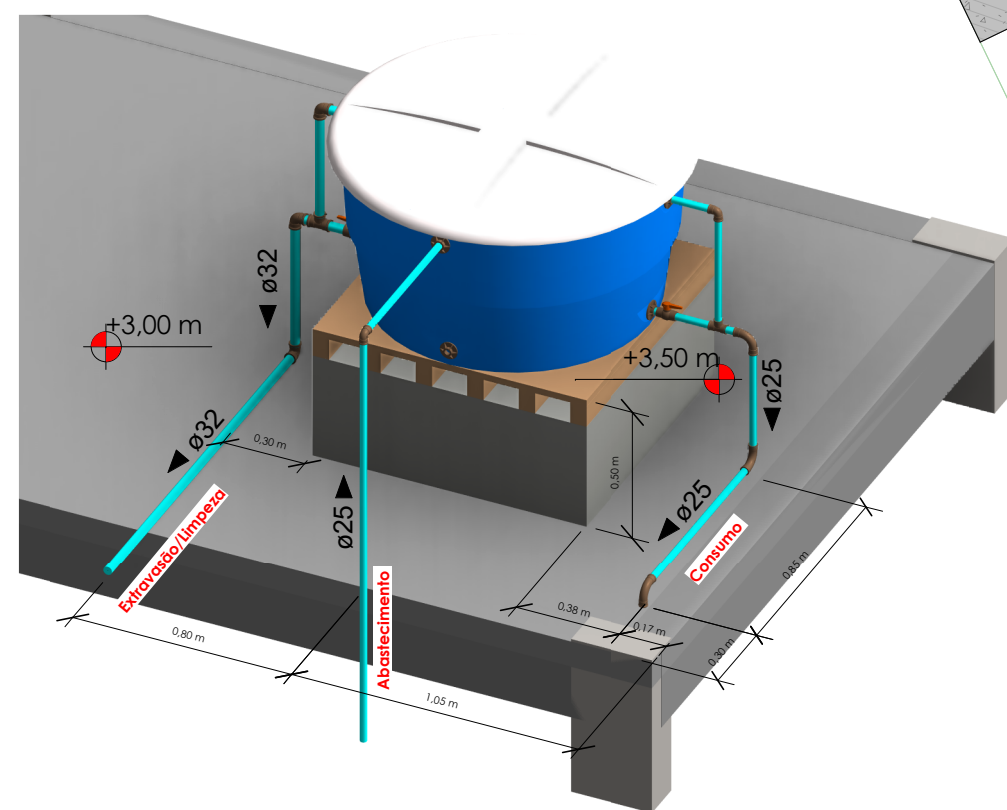

ISOMÉTRICA 02 - CAIXA_D'ÁGUA - ESC


1/25

LEGENDA - TUBULAÇÕES

- ESGOTO - ÁGUAS CINZAS
- ESGOTO - ÁGUAS NEGRAS
- ÁGUA FRIA
- VENTILAÇÃO
- ÁGUA QUENTE


PLANTA BAIXA _CAIXA_D'ÁGUA - ESC

1/20

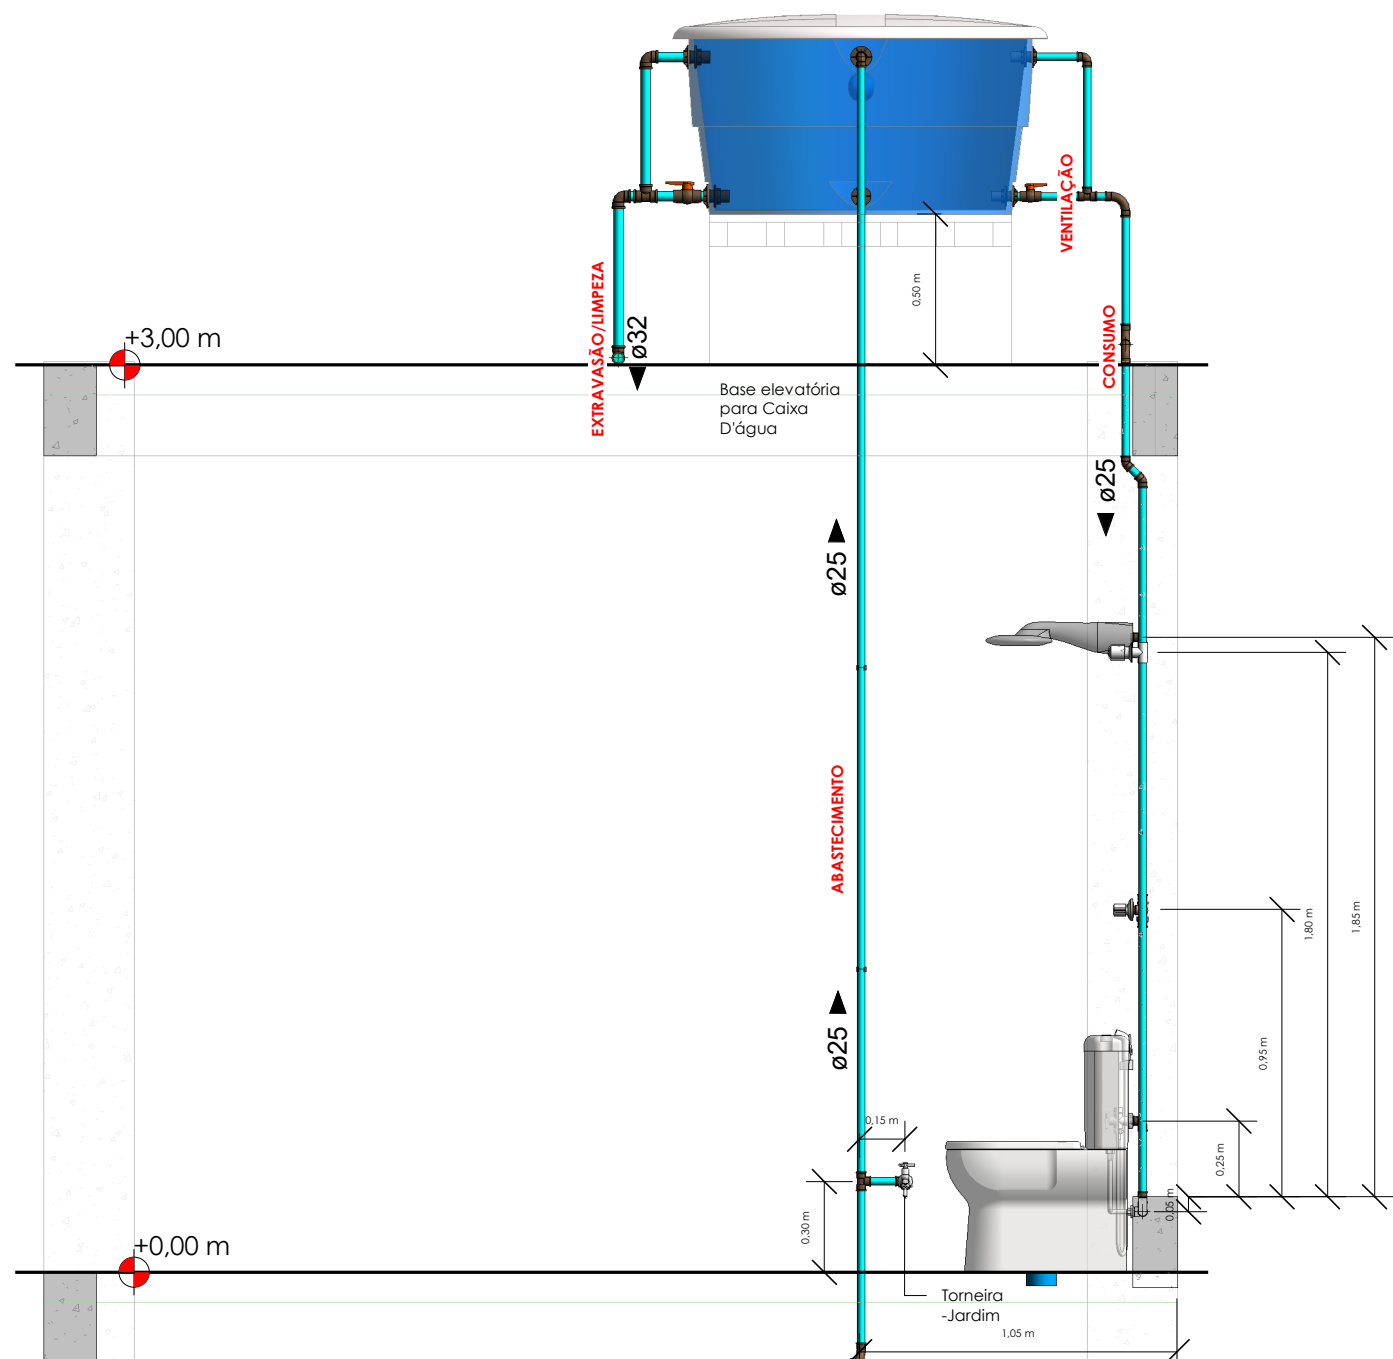

CORTE AA

ESC 1/25

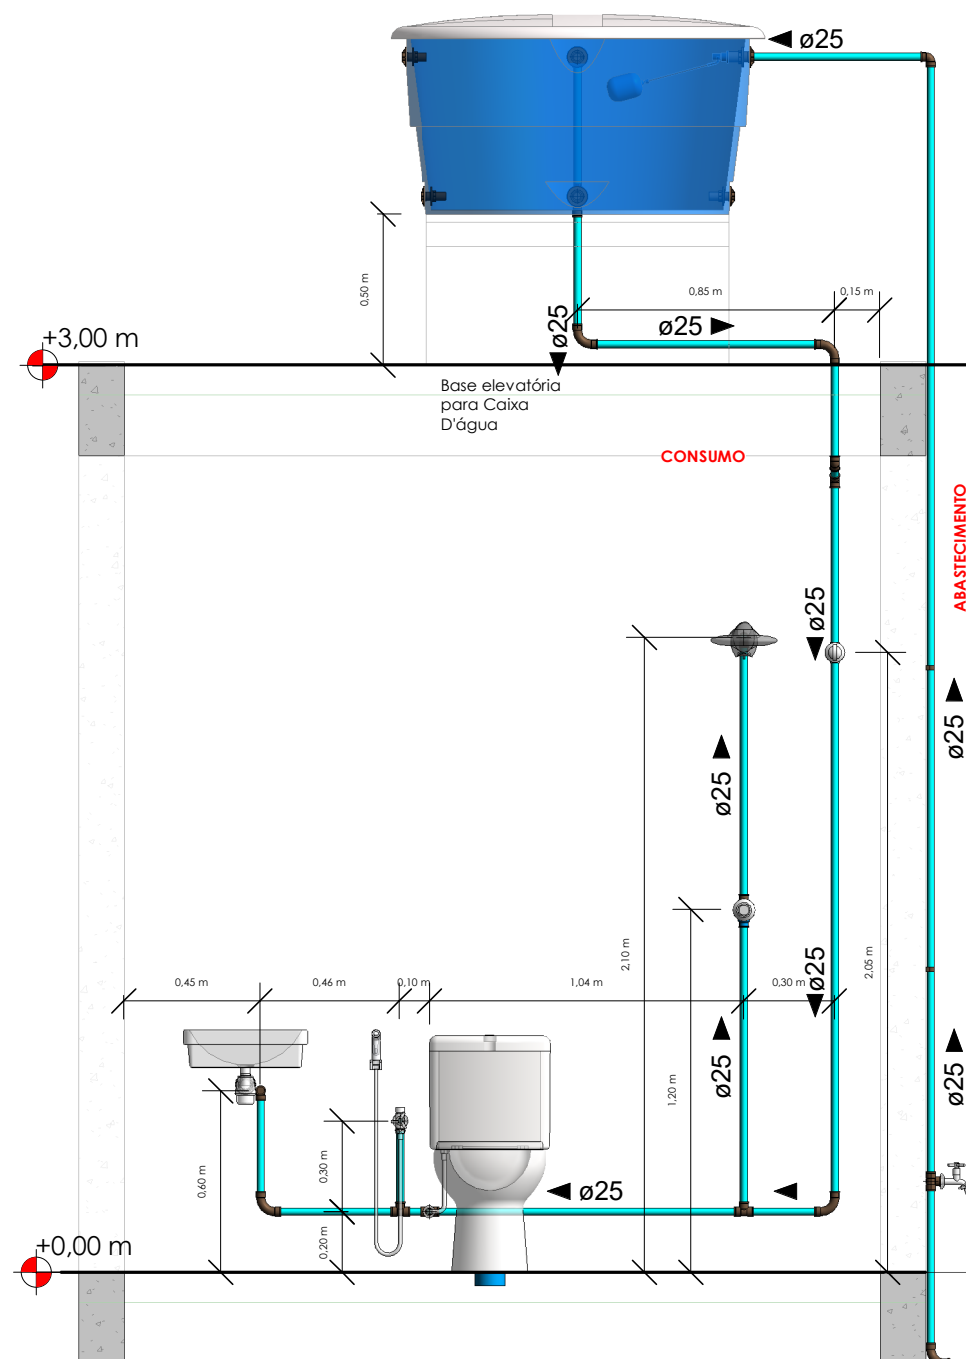

CORTE BB

ESC 1/25

PROPRIETÁRIO: PREFEITURA MUNICIPAL DE COREMAS - PB

PROJETO: LINCOLN CARTAXO DE LIRA JÚNIOR CREA 160.814.689-8

PROJETO: INSTALAÇÕES HIDRÁULICAS, GUARITA - PRAÇA NOVA COREMAS

CONCEDENTE: PREFEITURA MUNICIPAL DE COREMAS - PB

CONVENIENTE: MUNICÍPIO DE COREMAS - PB

LOCAL: COREMAS - PB

		RESPONSÁVEL TÉCNICO	RUBRICA	DADOS
DATA	24/04/2025	LINCOLN CARTAXO		CREA 160.814.689-8
CÓPIA				
VISTO				

PRANCHA: 03 / 03

DESCRIÇÃO: PLANTA BAIXA - CAIXA D'ÁGUA CORTES E ISOMÉTRICAS

ESCALA: INDICADA



Av. Gov. Flavio R. Coutinho, 500, sl. 601
Jd. Oceania, 58037-005 - João Pessoa (PB)
Tel +55 99924.4447
e-mail: contato@lclprojetos.com