




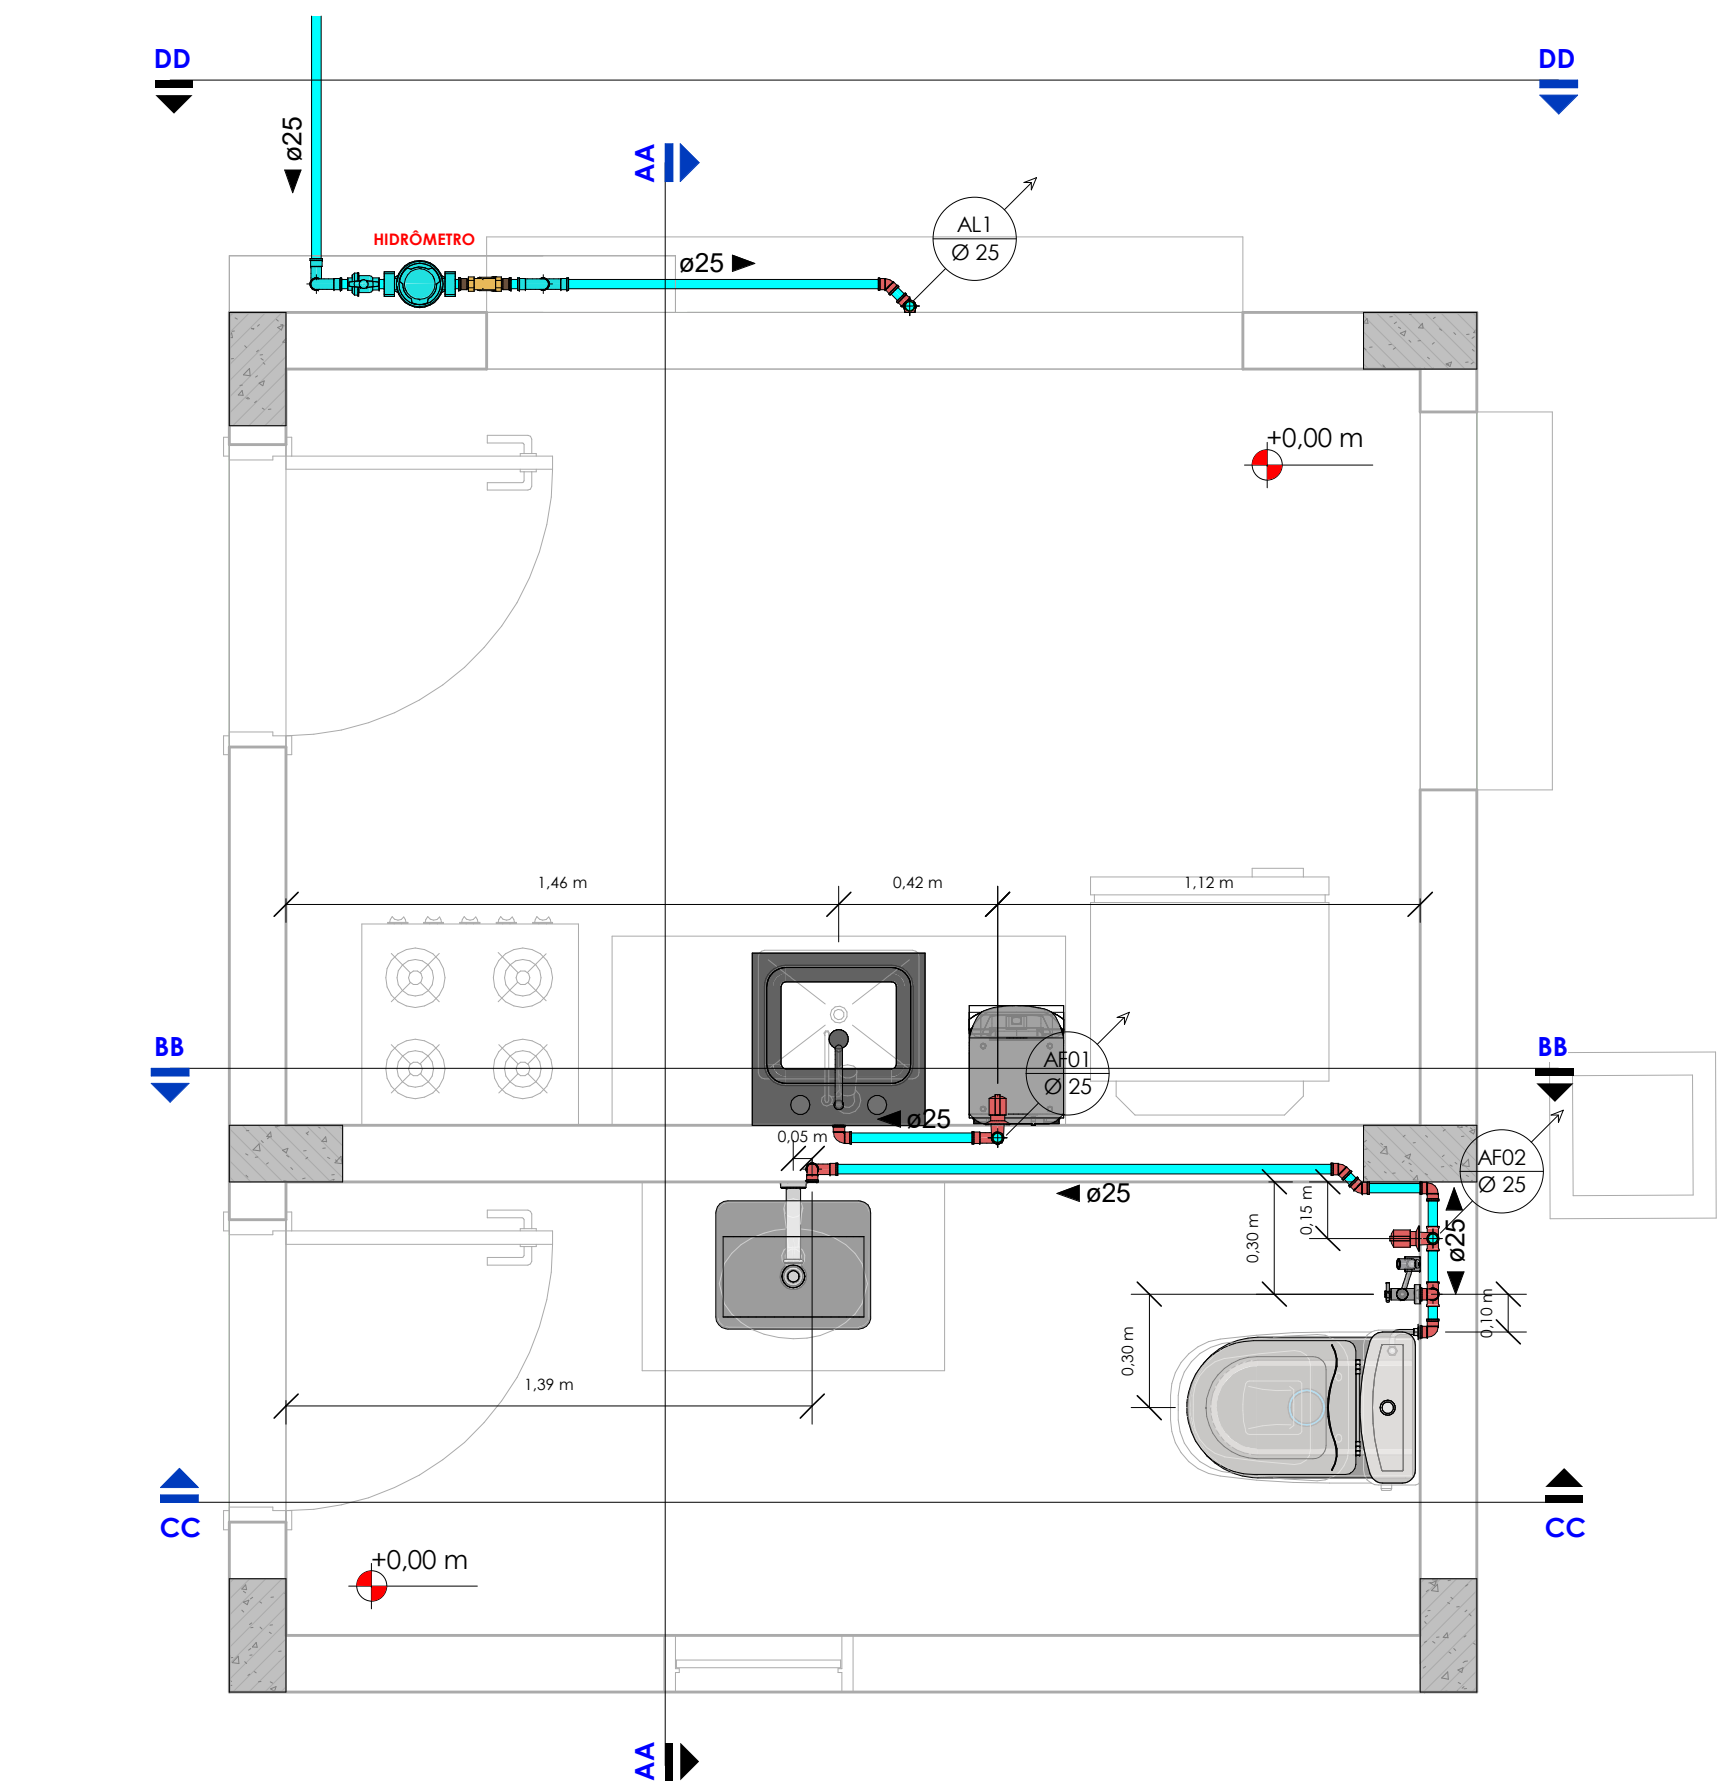


PLANTA BAIXA_TÉRREO QUIOSQUE_PRAÇA_NOVA_COREMAS - ESC 1/20

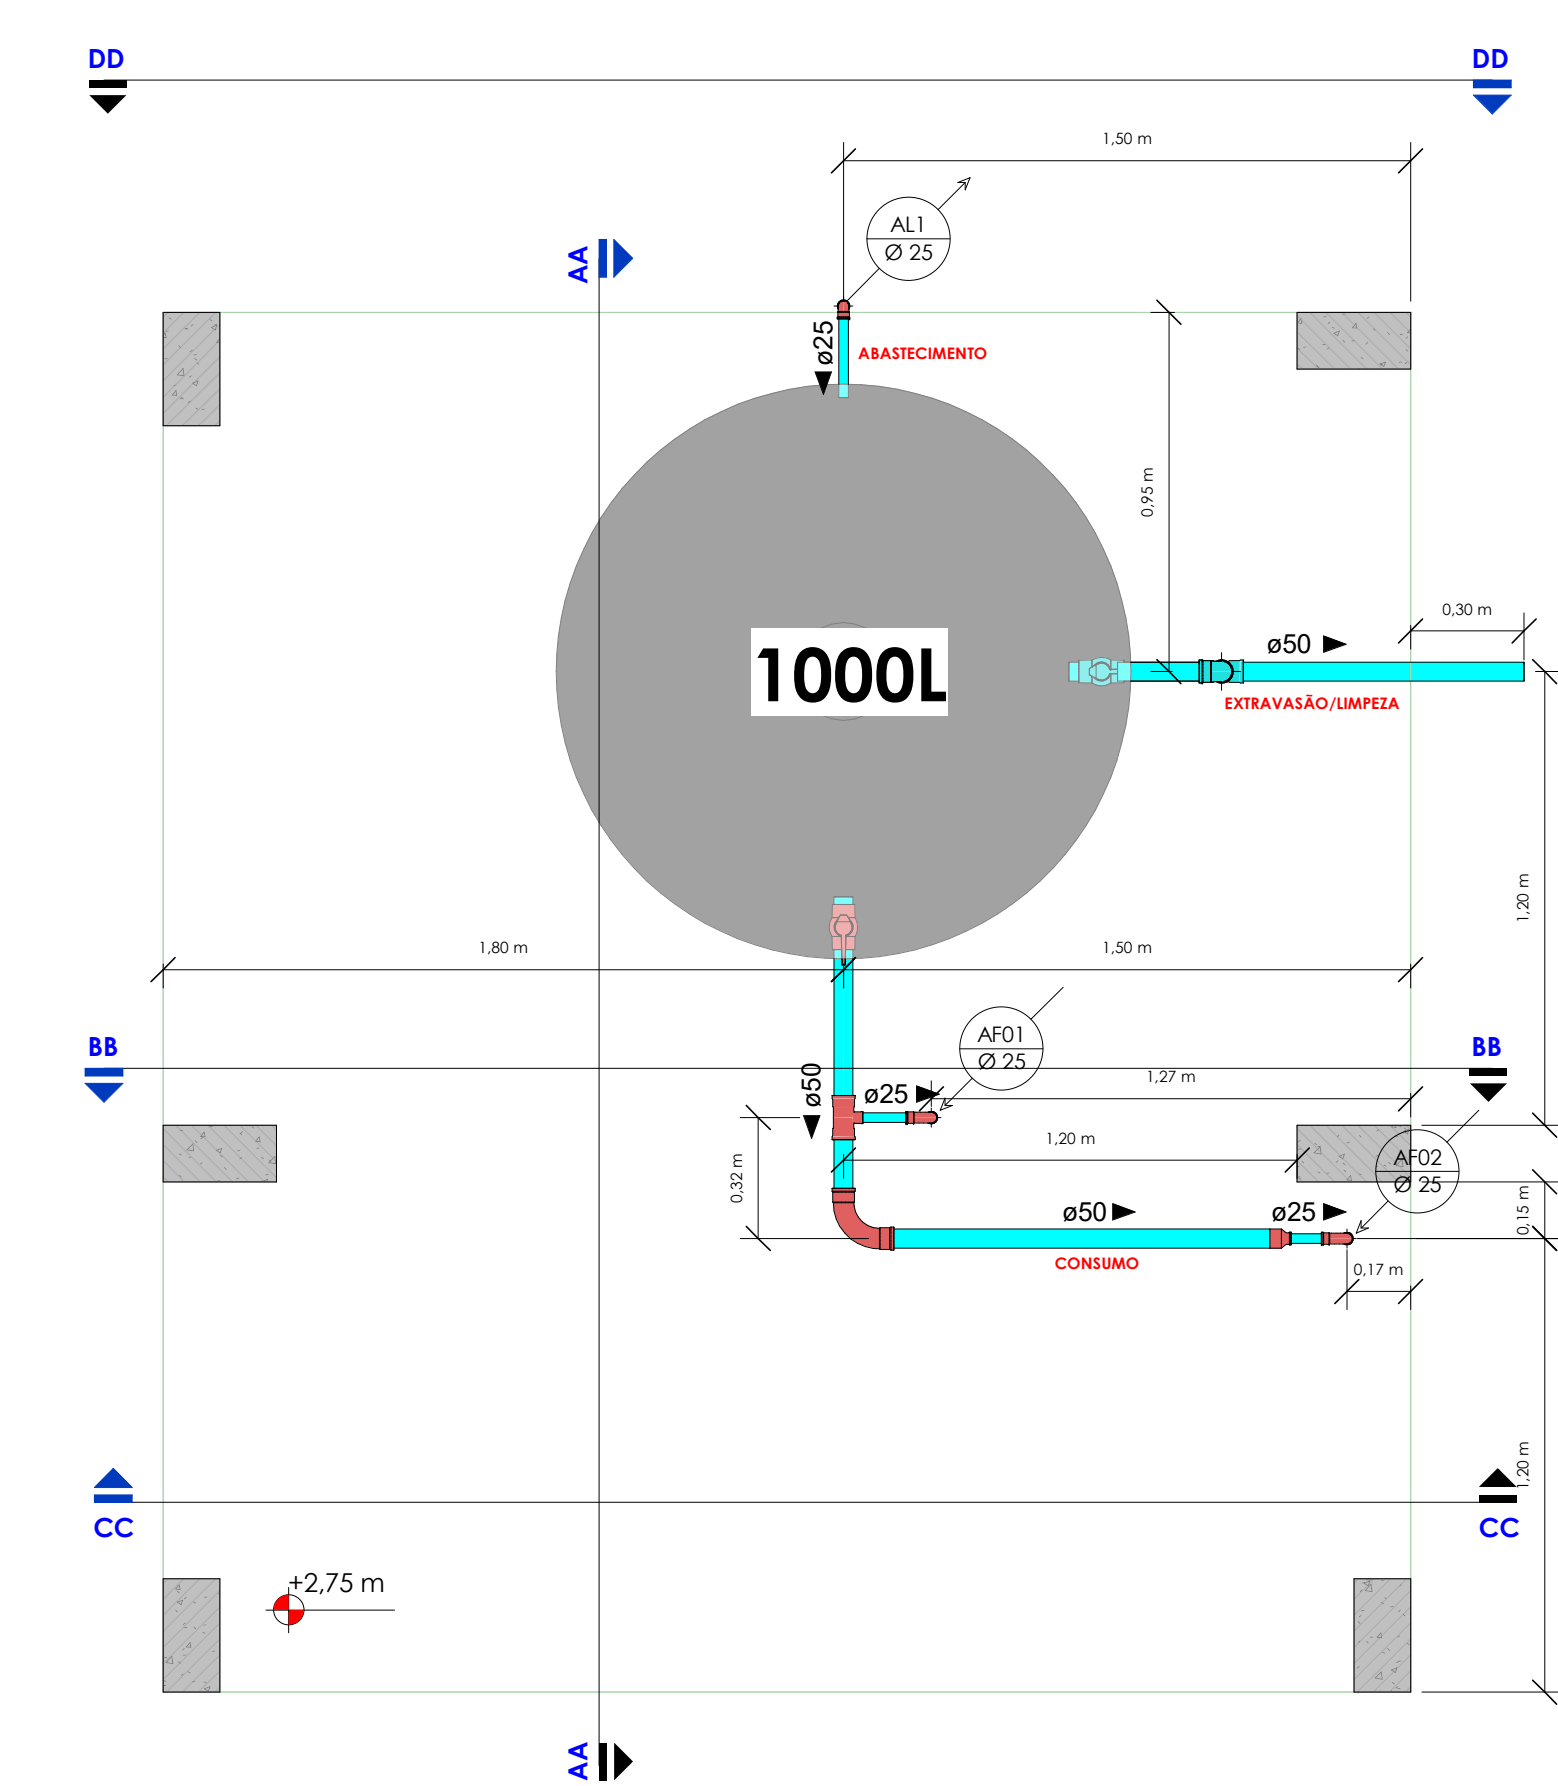

PLANTA BAIXA_COBERTA - CAIXA_D'ÁGUA - ESC 1/20

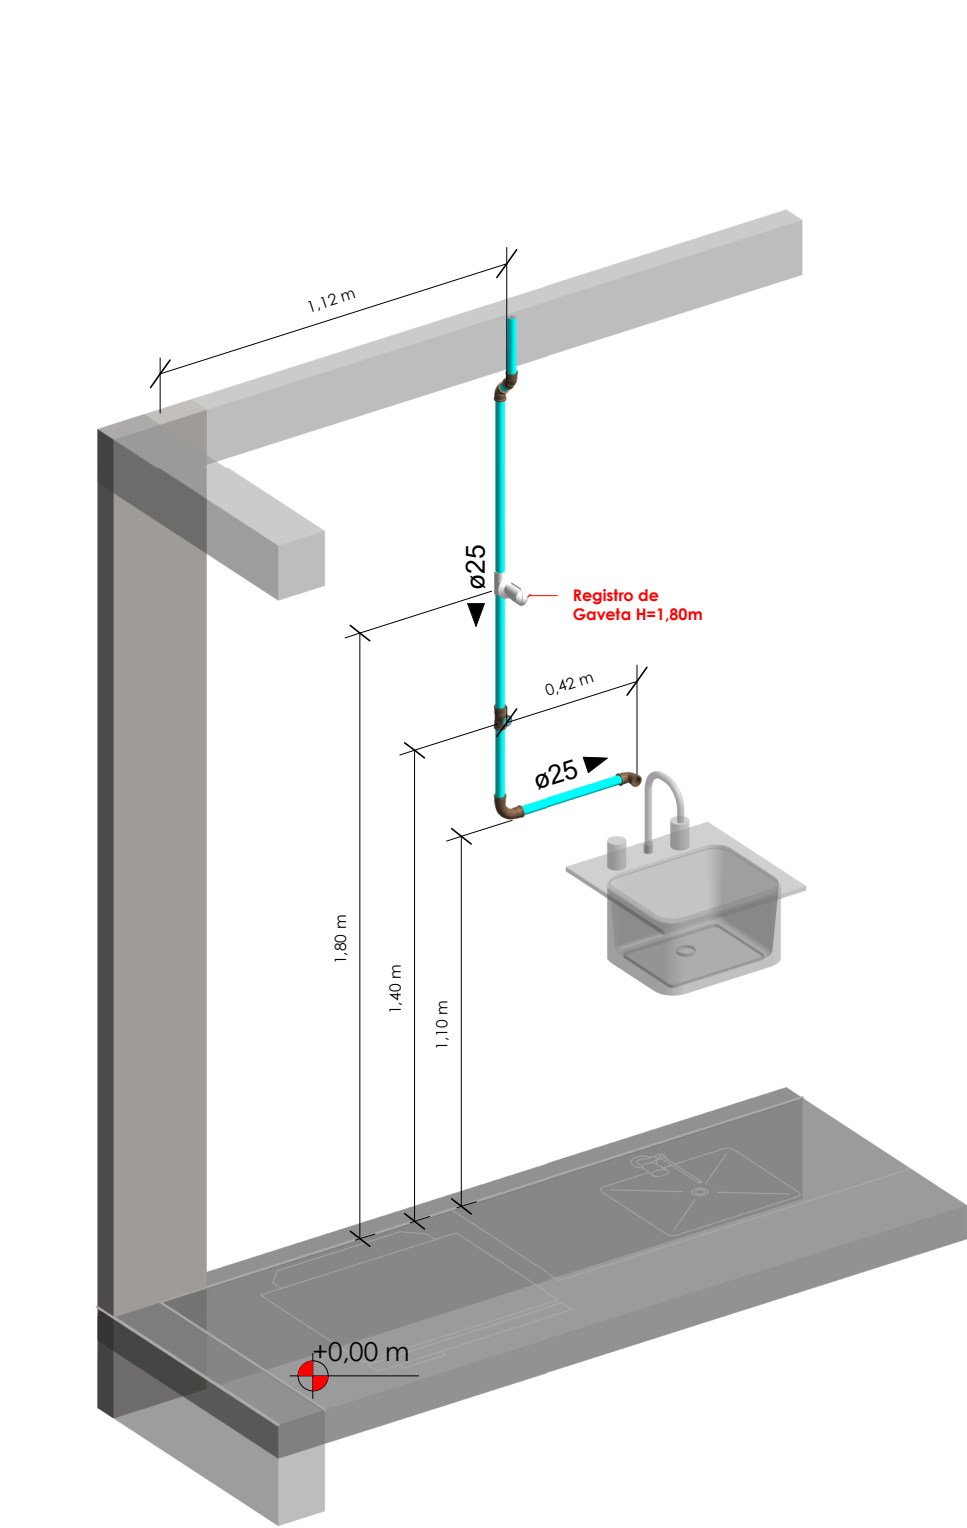

ISOMÉTRICA 02 - COZINHA - ESC 1/20

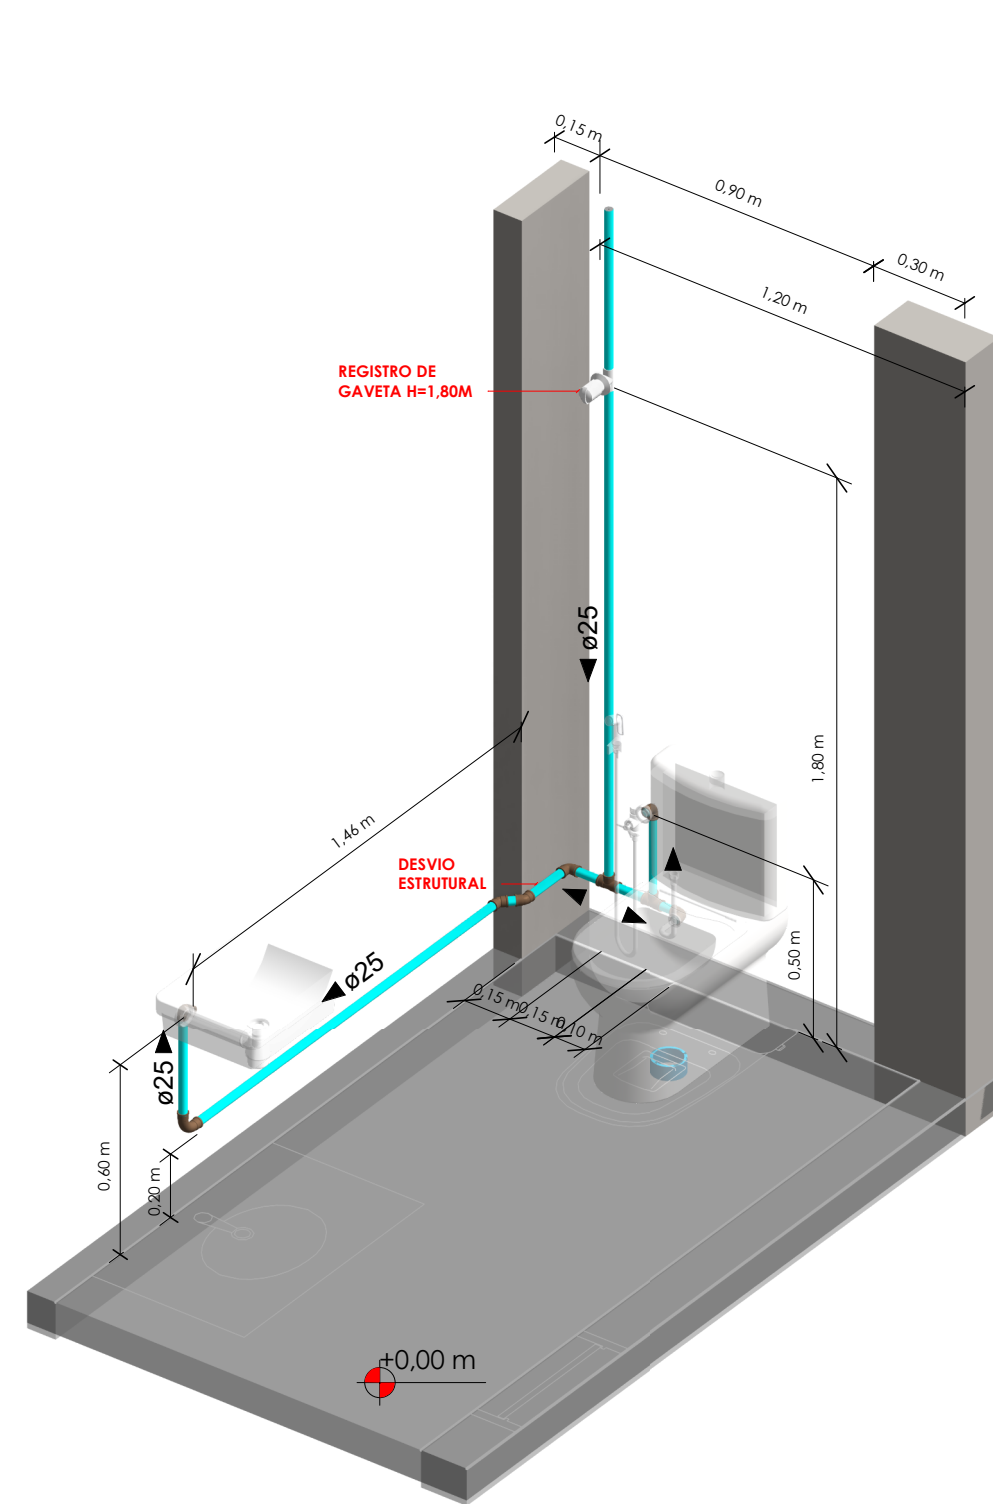

ISOMÉTRICA 01 - LAVABO - ESC 1/20

LEGENDA:


- TUBULAÇÃO PVC BRANCO - ESGOTO
- TUBULAÇÃO PVC BRANCO SN - VENTILAÇÃO ESGOTO
- TUBULAÇÃO PVC MARROM - ÁGUA FRIA
- AL-nn
Øxx
-ALIMENTAÇÃO DO RESERV. SUPERIOR
nn: número da coluna
xx: diâmetro nominal da coluna
- CV-nn
Øxx
-COLUNA DE VENTILAÇÃO
nn: número da coluna
xx: diâmetro nominal da coluna
- AF-nn
Øxx
-COLUNA DE ÁGUA FRIA (BARRILETE)
nn: número da coluna
xx: diâmetro nominal da coluna

LEGENDA - TUBULAÇÕES


- ESGOTO - ÁGUAS CINZAS
- ESGOTO - ÁGUAS NEGRAS
- ÁGUA FRIA
- VENTILAÇÃO
- ÁGUA QUENTE

TABELA DE ALTURAS


SIGLA	PONTO	ALTURA
CH	CHUVEIRO	2,10 m
LV	LAVATÓRIO	0,95 m
VS	VASO SANITÁRIO	0,20 m
RG	REGISTRO DE GAVETA	1,80 m
RP	REGISTRO DE PRESSÃO	1,20 m
PIA	PIA DE COZINHA	0,90 m
TQ	TANQUE	1,10 m

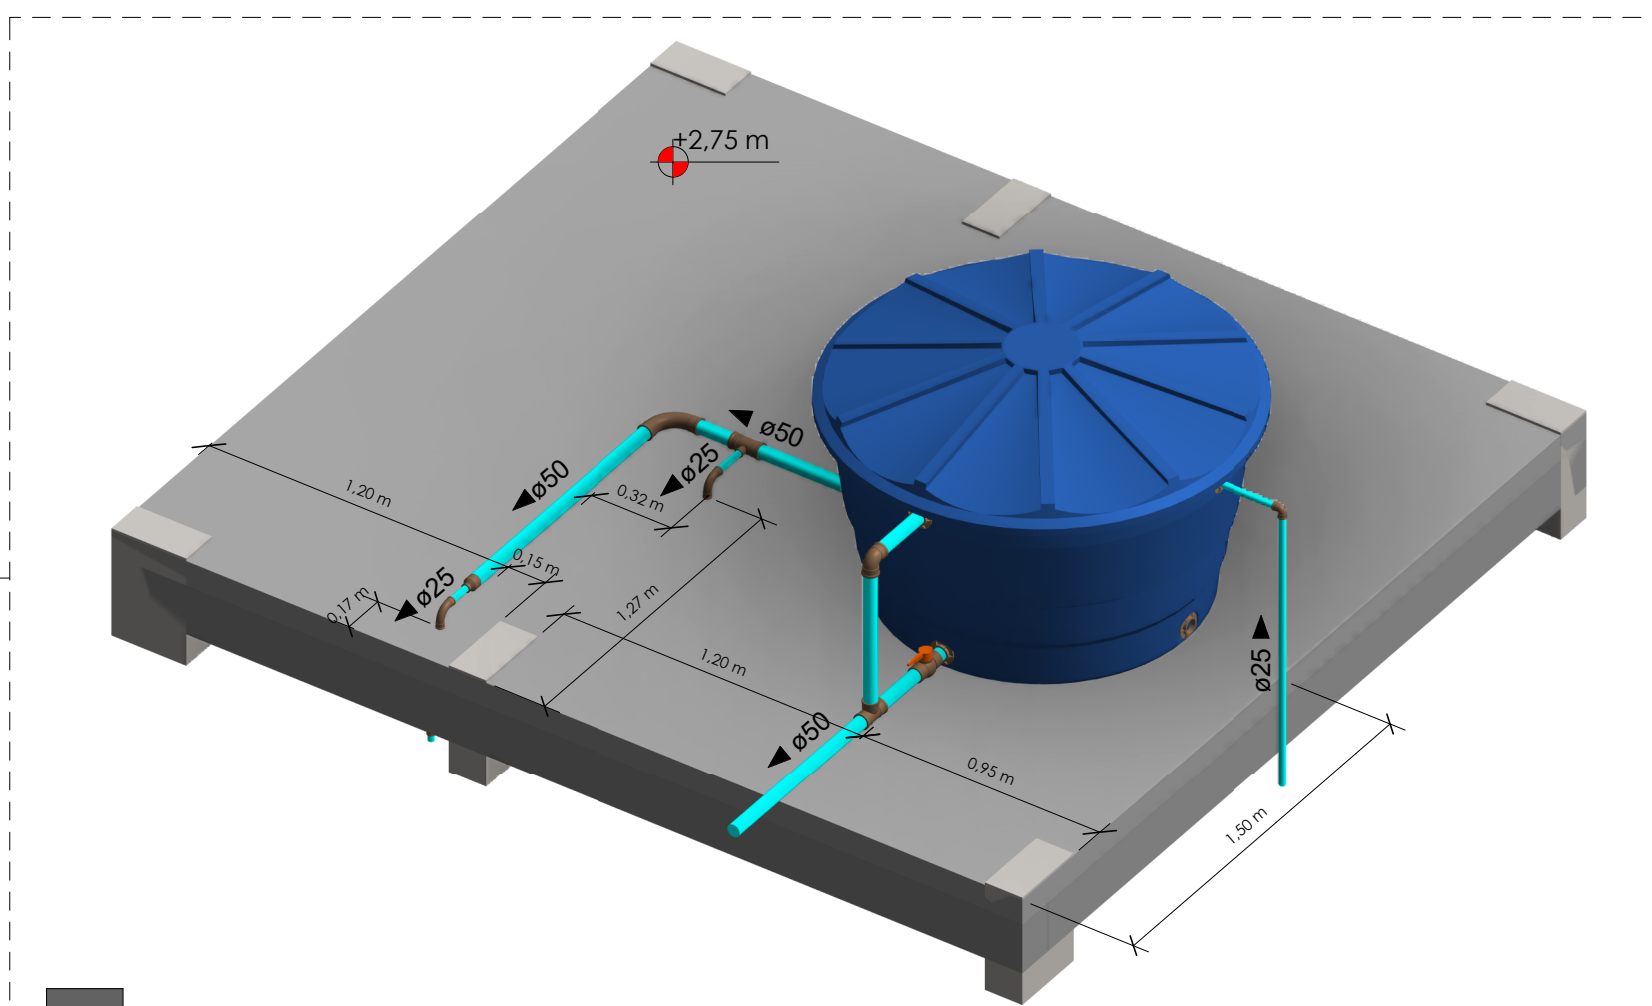


ISOMÉTRICA 03 - CAIXA D'ÁGUA - ESC 1/25

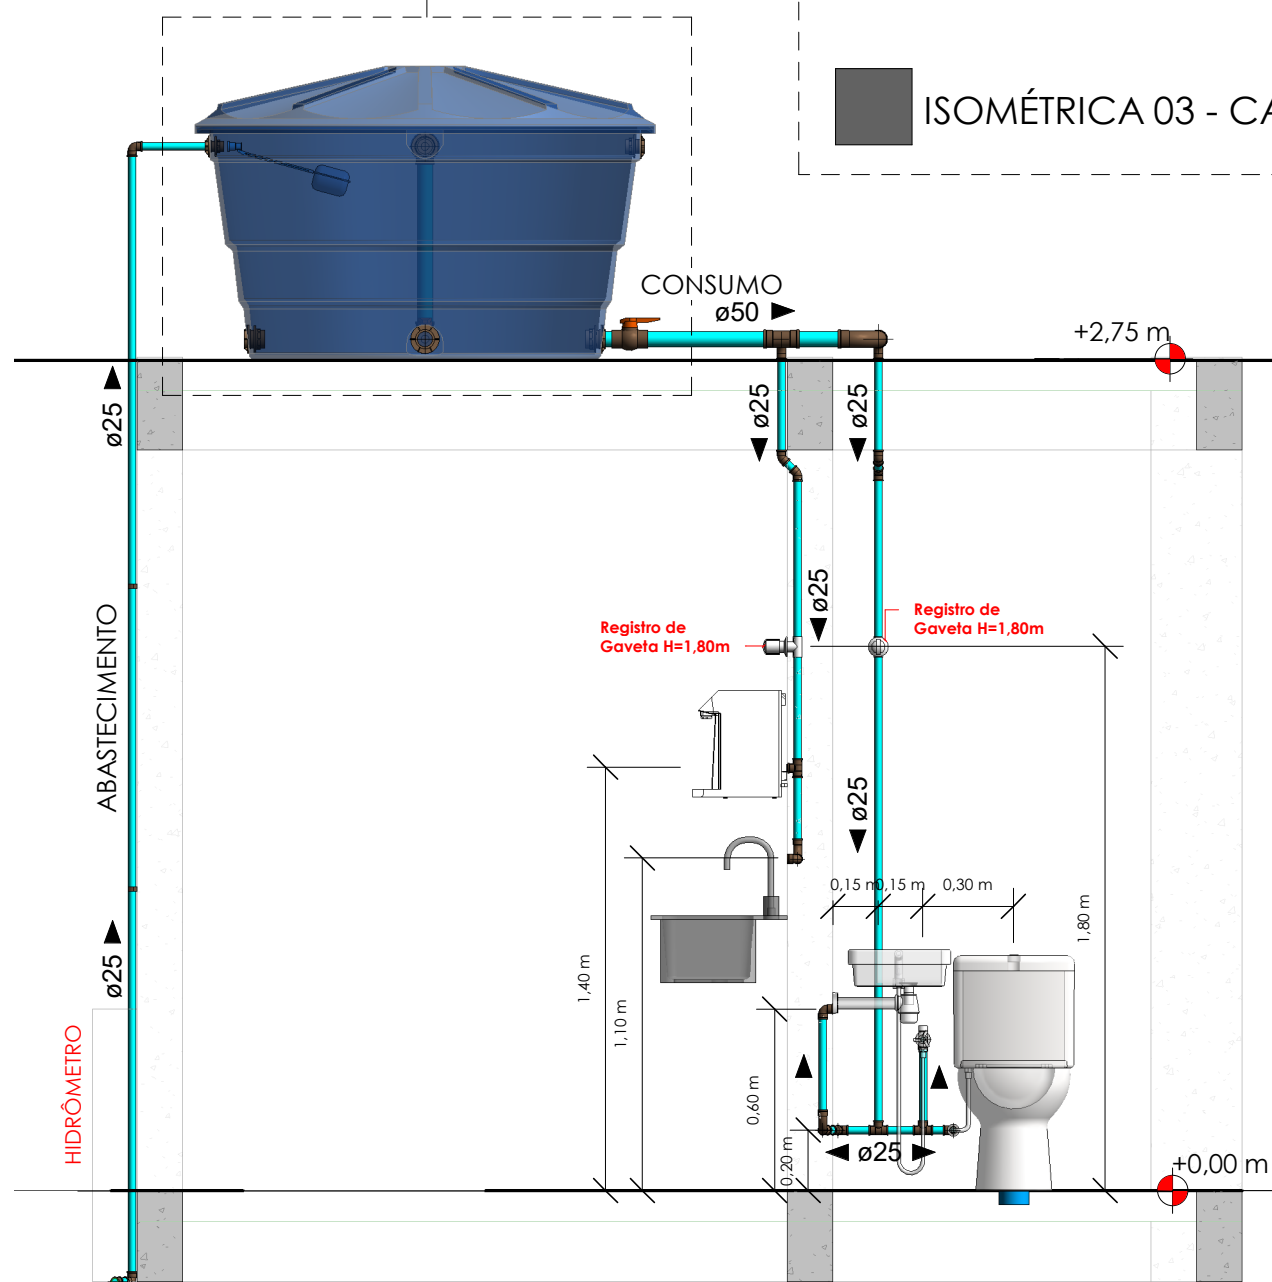


CORTE AA ESC 1/25

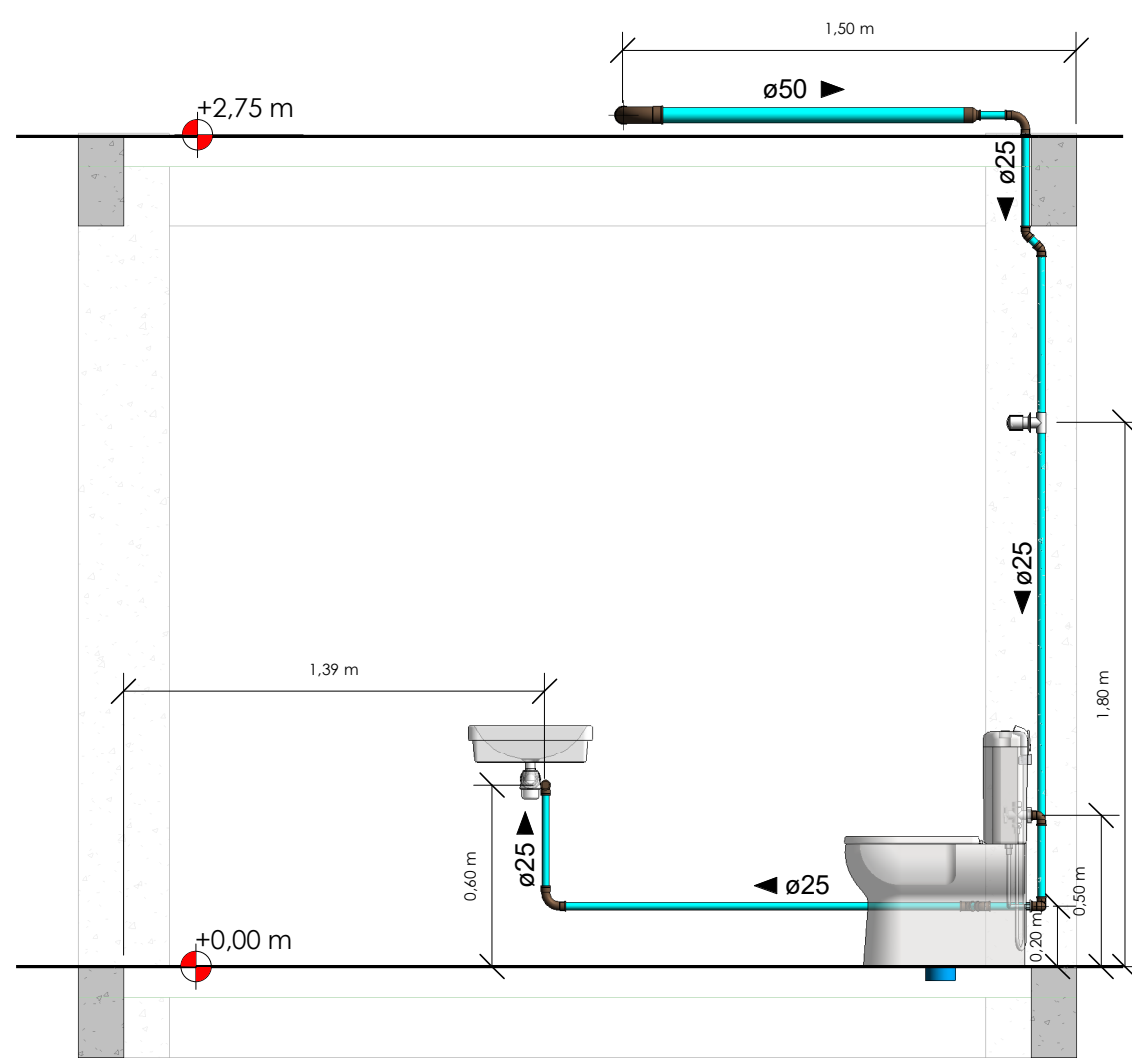

CORTE CC ESC 1/25

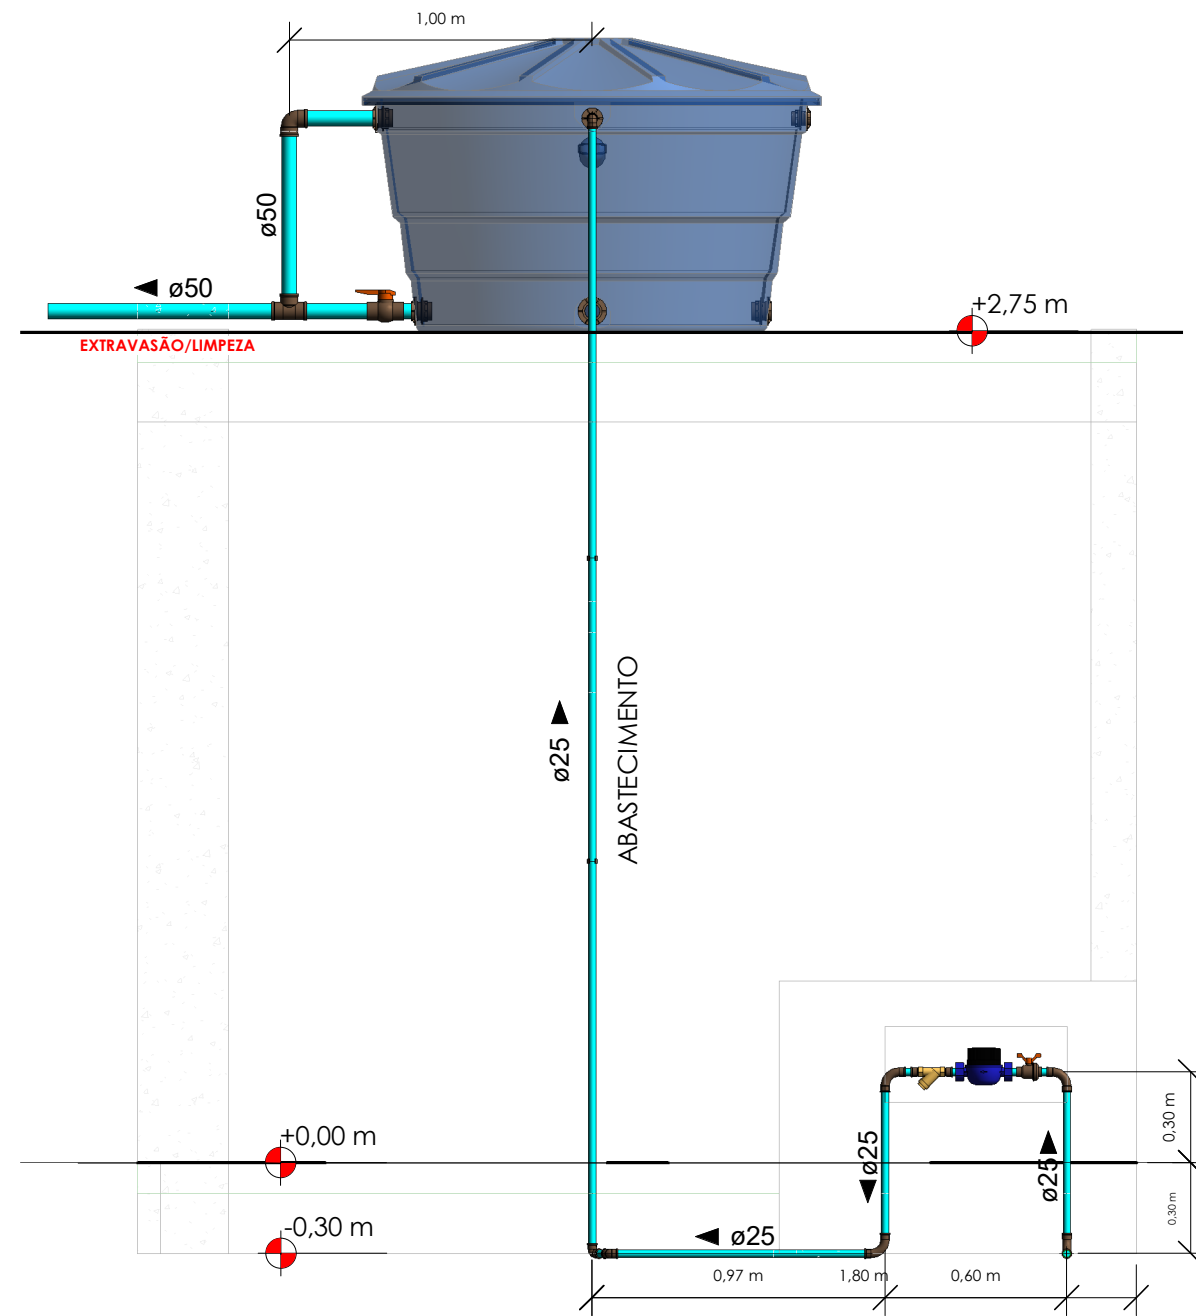

CORTE DD ESC 1/25

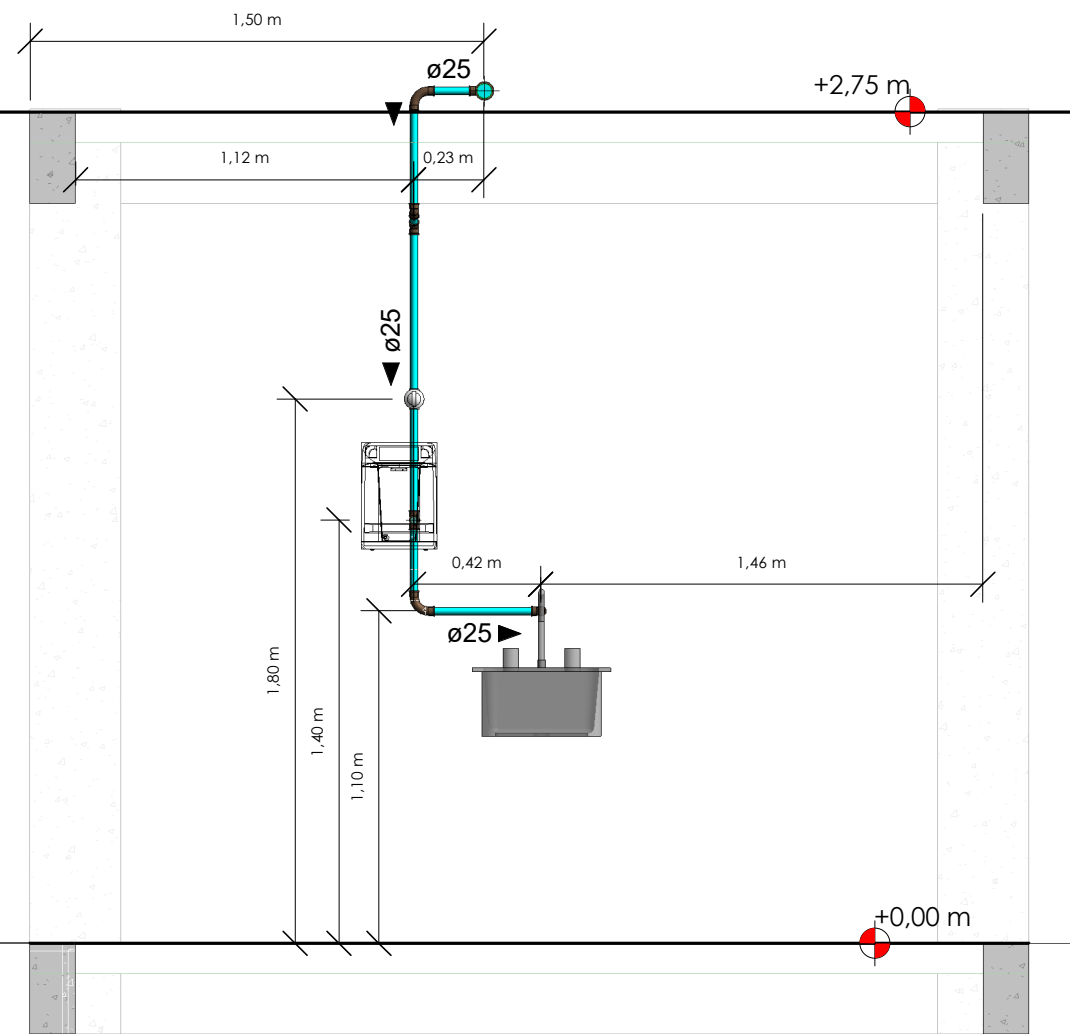

CORTE BB ESC 1/25

LINCOLN CARTAXO DE LIRA
JUNIOR:06897861405

Assinado de forma digital por
LINCOLN CARTAXO DE LIRA
JUNIOR:06897861405
Dados: 2025.04.28 11:37:47 -03'00'

PROPRIETÁRIO: PREFEITURA MUNICIPAL DE COREMAS - PB

PROJETO: LINCOLN CARTAXO DE LIRA JÚNIOR CREA 160.814.689-8

CONCEDENTE: PREFEITURA MUNICIPAL DE COREMAS - PB
CONVENIENTE: MUNICÍPIO DE COREMAS - PB
LOCAL: COREMAS - PB

PRANCHA: 02 / 01
DESCRIÇÃO: PLANTA BAIXA TÉRREO E CAIXA D'ÁGUA
CORTES E ISOMÉTRICAS
ESCALA: INDICADA

Av. Gov. Flavio R. Coutinho, 500, sl. 601
Jd. Oceania, 58037-005 - João Pessoa (PB)
Tel +55 99924.4447
e-mail: contato@lclprojetos.com